


BẢN ĐỒ HIỆN TRẠNG

KHOANH VÙNG CÁC KHU VỰC BẢO VỆ DI TÍCH CHÙA VĨNH THƯỢNG

- Chủ đầu tư : Ban Quản lý Di tích Danh thắng Hà Nội
- Địa điểm : Xã Sơn Công - huyện Ứng Hòa - thành phố Hà Nội
- Diện tích : 8.150,1 m² giới hạn bởi các điểm từ 1 đến 17, 1.

TP. HÀ NỘI - H. ỨNG HÒA

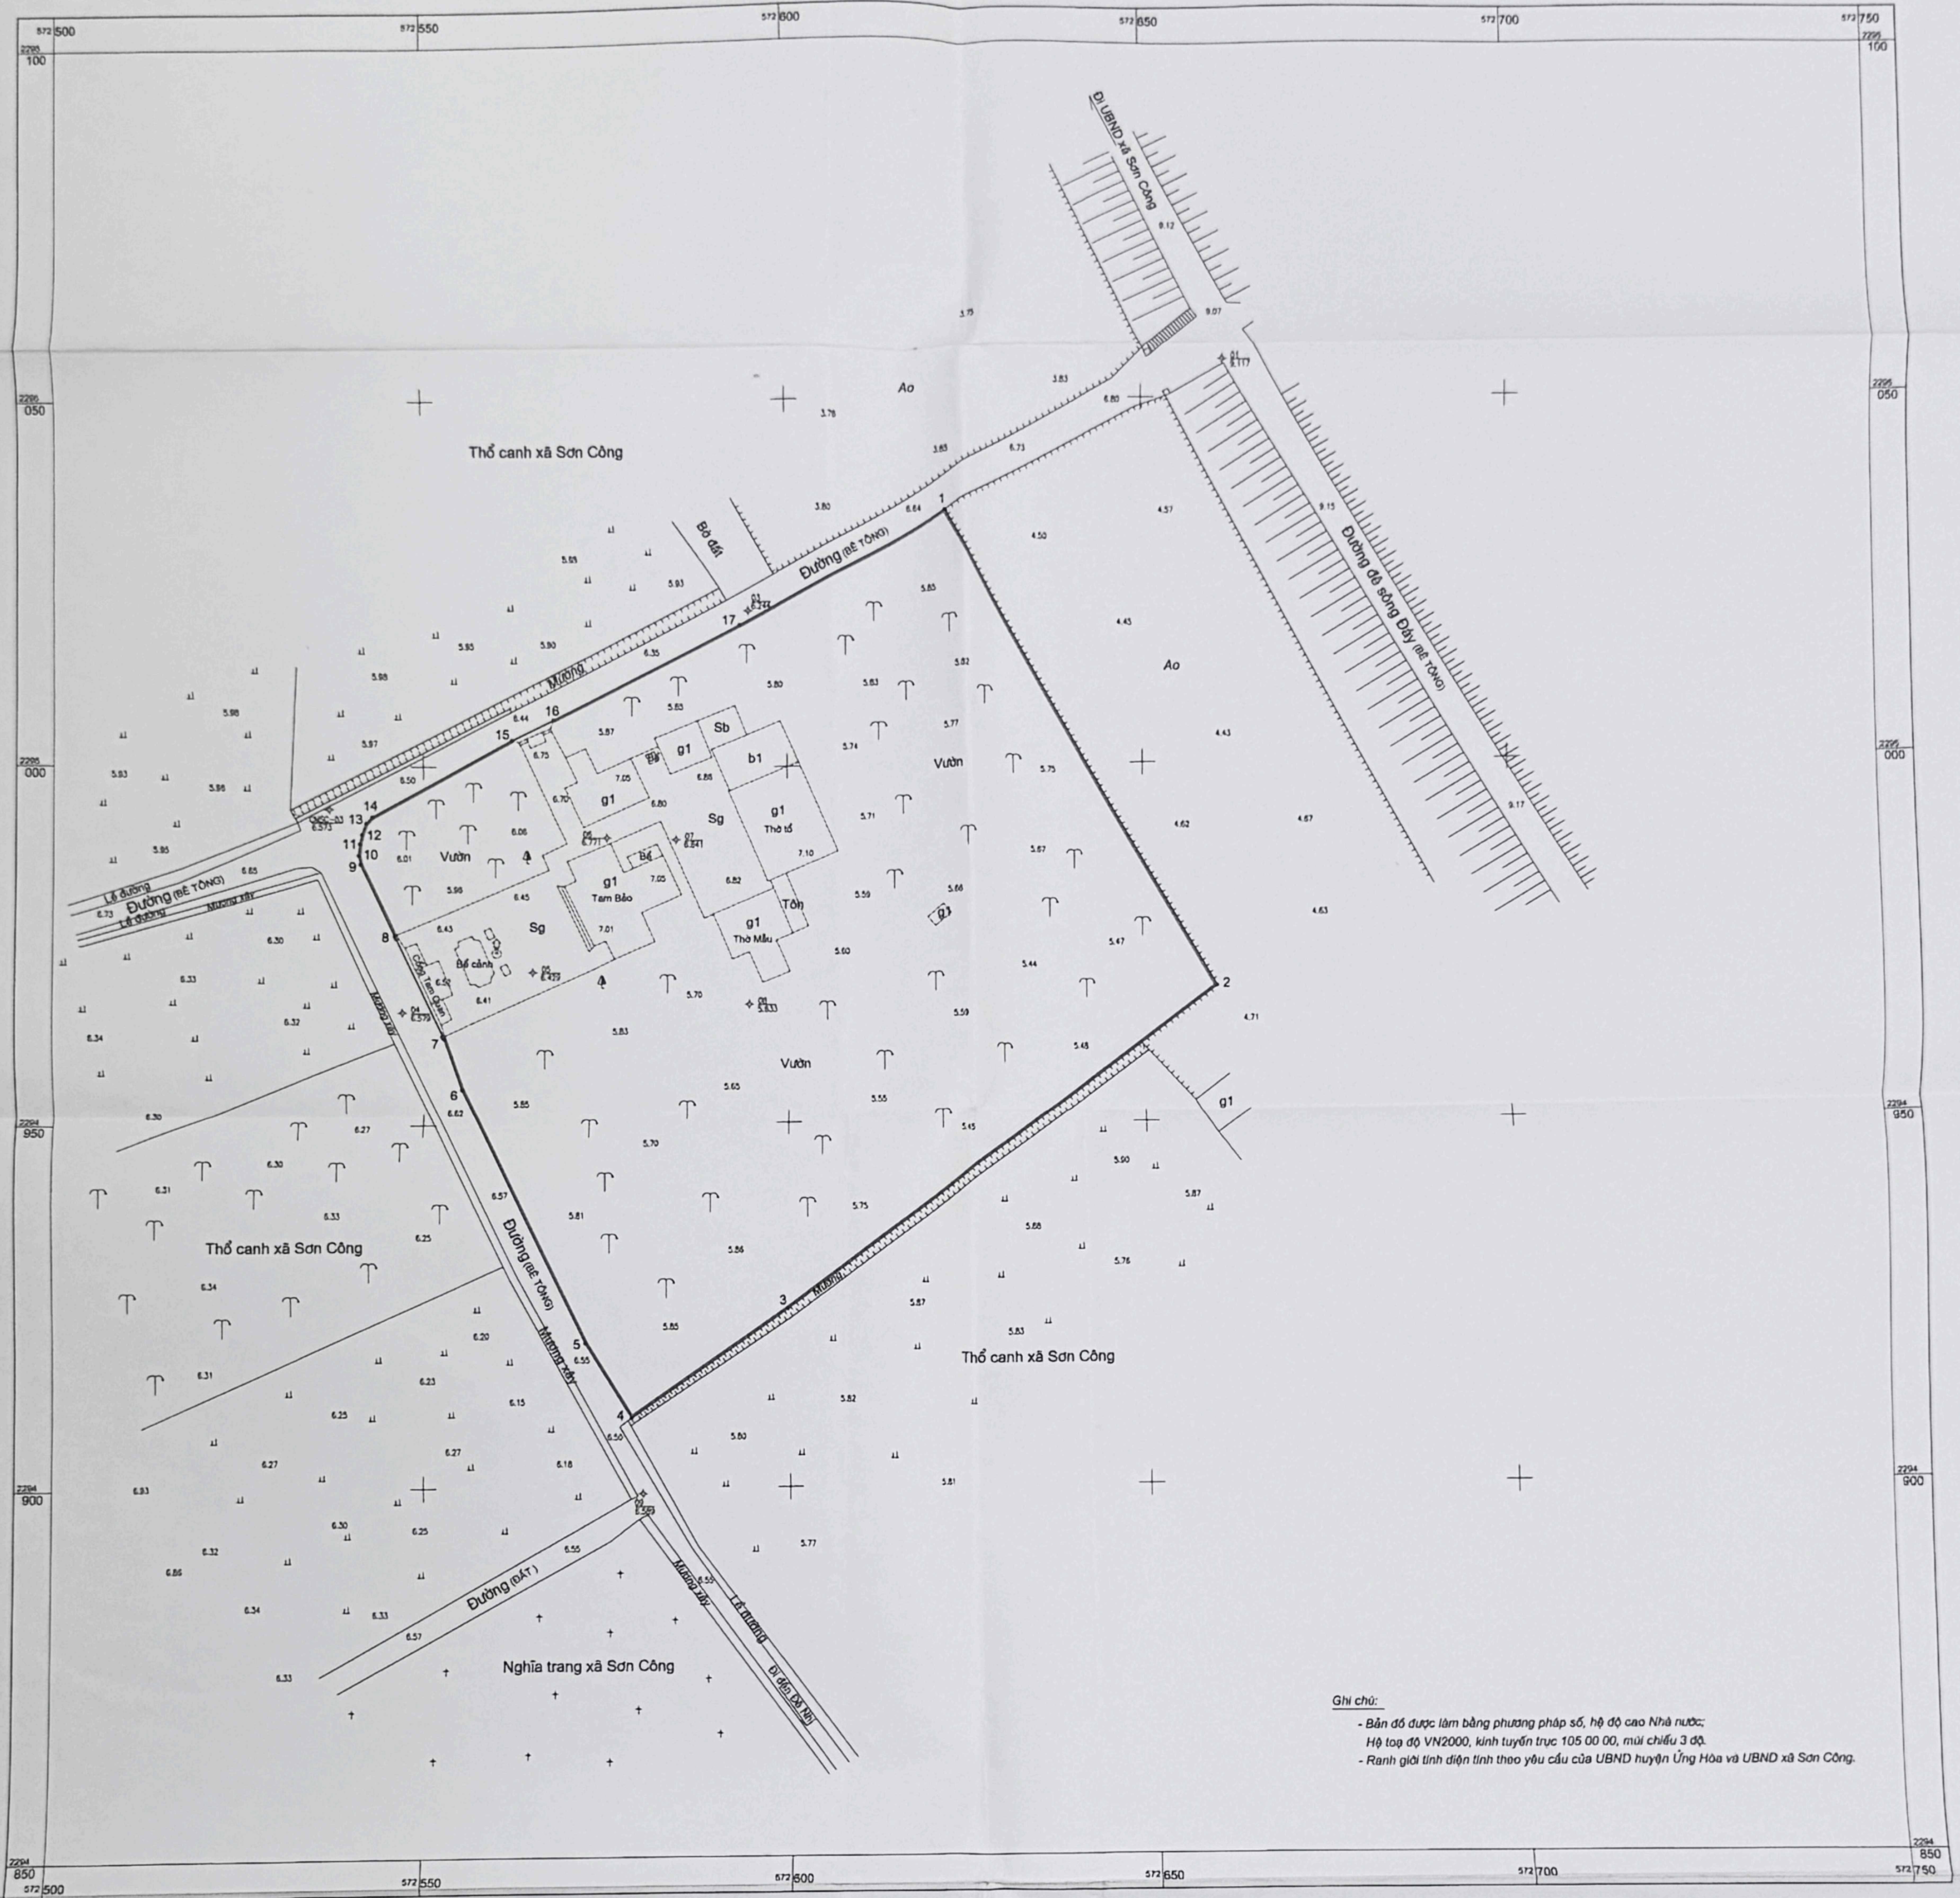

Ghi chú:
- Bản đồ được làm bằng phương pháp số, hệ độ cao Nhà nước;
- Hệ tọa độ VN2000, kinh tuyến trục 105 00 00, múi chiếu 3 độ;
- Ranh giới tính diện tích theo yêu cầu của UBND huyện Ứng Hòa và UBND xã Sơn Công.

Số hợp đồng : /HDKT
Số bản đồ : XN5 -

Đo vẽ tháng 9 năm 2018
Công ty cổ phần Địa chính Hà Nội
Phó Tổng giám đốc



TỶ LỆ 1:500

1 cm trên bản đồ bằng 5 m trên thực địa

10m 5 0 10 20 30 40

Sở Tài nguyên và Môi trường Hà Nội cùng các cơ quan liên quan thống nhất hiện trạng khoanh vùng bảo vệ di tích Chùa Vĩnh Thượng xã Sơn Công, huyện Ứng Hòa, thành phố Hà Nội theo Biên bản khoanh vùng các khu vực bảo vệ di tích ngày 7/9/2018...

Kiểm tra ngày 09 tháng 10 năm 2018
Phòng Đo đạc, Bản đồ và Viễn thám

Nguyễn Duy Hùng

Xác nhận ngày tháng năm 2018
Sở Tài nguyên và Môi trường Hà Nội

KT. Giám đốc
Phó Giám đốc
Nguyễn Minh Mười

ỦY BAN NHÂN DÂN THÀNH PHỐ HÀ NỘI	SỞ VĂN HÓA VÀ THỂ THAO HÀ NỘI	BAN QUẢN LÝ DI TÍCH DANH THẮNG HÀ NỘI	UBND HUYỆN ỨNG HÒA	PHÒNG TÀI NGUYÊN VÀ MÔI TRƯỜNG HUYỆN ỨNG HÒA	PHÒNG VĂN HÓA VÀ THÔNG TIN HUYỆN ỨNG HÒA	UBND XÃ SƠN CÔNG
 PHÓ CHỦ TỊCH Ngô Văn Quý	 TRƯỞNG BAN Nguyễn Minh Tiến	 TRƯỞNG BAN Nguyễn Đoàn Văn	 PHÓ CHỦ TỊCH Hoàng Đức Lan Anh	 PHÓ PHÒNG Vũ Thị Cảnh	 Đang Đăng Khoa	 PHÓ CHỦ TỊCH Nguyễn Quang Vinh